PROJECT

Dennis Bunch

Designed by Premium Pergola LLC.

455 Central Ave 2nd Floor, Cedarhurst, NY 11516

Address:

MODEL

Main System : PERGOLA

Side Systems :Screen

ADDITIONAL

L Angle 20mmX40mm 18 pcs. Sukkah Braket 0 pcs. 55mmx105mm

L Angle 20mmX100mm 9 pcs.

Spray Paint:2 pc.

All posts have to be 4" extra All screens have to be 4" extra

COLOURS

Structure :

Louver Blade :

Pergola Fabric :

Screen Fabric :

Structure	Louver Blade

Pergola Fabric	Screen Fabric

GLASS TYPE

Glass Type : Temp. Laminated / Clear Temp. / Clear Temp.

Inner : Fix W. : 5/32"

Air Space : 5/8"

Exterior : 5/32 "

SPECS.

Front Pillar: Back Beam:

Back Pillar: Side Beam:

Side Pillar: Beam: for ...

Installation Type : ☐ Wall ☐ Ceiling ■ Freestanding

LIGHTING

Tube LED :	pcs.	■ Yes	☐ No
Spot LED :	pcs.	☐ Yes	☐ No
Perimeter LED light :		☐ Yes	☐ No
Quantity of LED :	pcs.	☐ Yes	☐ No
Reciever : Dimmer Unit		■ Yes	☐ No pc

ELECTRICAL OPERATION

Electric Power:	☐ 220 V	■ 110 V	☐ 24 V	
Motor:		■ included	☐ not included	
Rem. Control :	☐ Telis-1	☐ Telis-4	■ Telis-16	1pc
Manual Crank Operation :		☐ Yes	■ No	
Panel Insulation (PU Foam)		☐ Yes	■ No	

REVISIONS

NO.	DESCRIPTION	DATE	BY

PREMIUM PERGOLA

CUSTOMER SIGNATURE:

DRAWN BY:

CHECKED BY:

Date: 12/23/2025

P-101

SPECIFICATIONS:

GLASS SCHEDULE:

1.

2.

HARDWARE SCHEDULE:

1.

2.

GENERAL NOTES:

1.

2.

ABBREVIATIONS:

F.S. = FRAME SIZE
R.O. = ROUGH OPENING
O.D. = OPENING/OVERALL DIMENSION
D.L.O. = DAY LIGHT OPENING

DRAWING INDEX:

PAGE NO:	DESCRIPTION
P101	GENERAL INFORMATIONS
P102	GENERAL INFORMATIONS
P103	PLAN
P104	ELEVATION
P105	ELEVATION
P106	LIGHT PLAN
P107	DETAIL
P108	DETAIL
P109	
P110	
P111	
P112	
P113	
P114	
P115	
P116	
P117	
P118	
P119	
P120	

SYMBOLS:

DETAIL CALLOUT

SECTION CALLOUT

ELEVATION CALLOUT

REVISION DELTA

GL-X

GLASS TAG

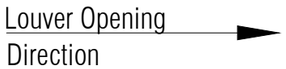

REVISIONS

NO.	DESCRIPTION	DATE	BY

PREMIUM PERGOLA

CUSTOMER SIGNATURE:

DRAWN BY:

CHECKED BY:

Date: 12/23/2025

P-102

PLAN VIEW

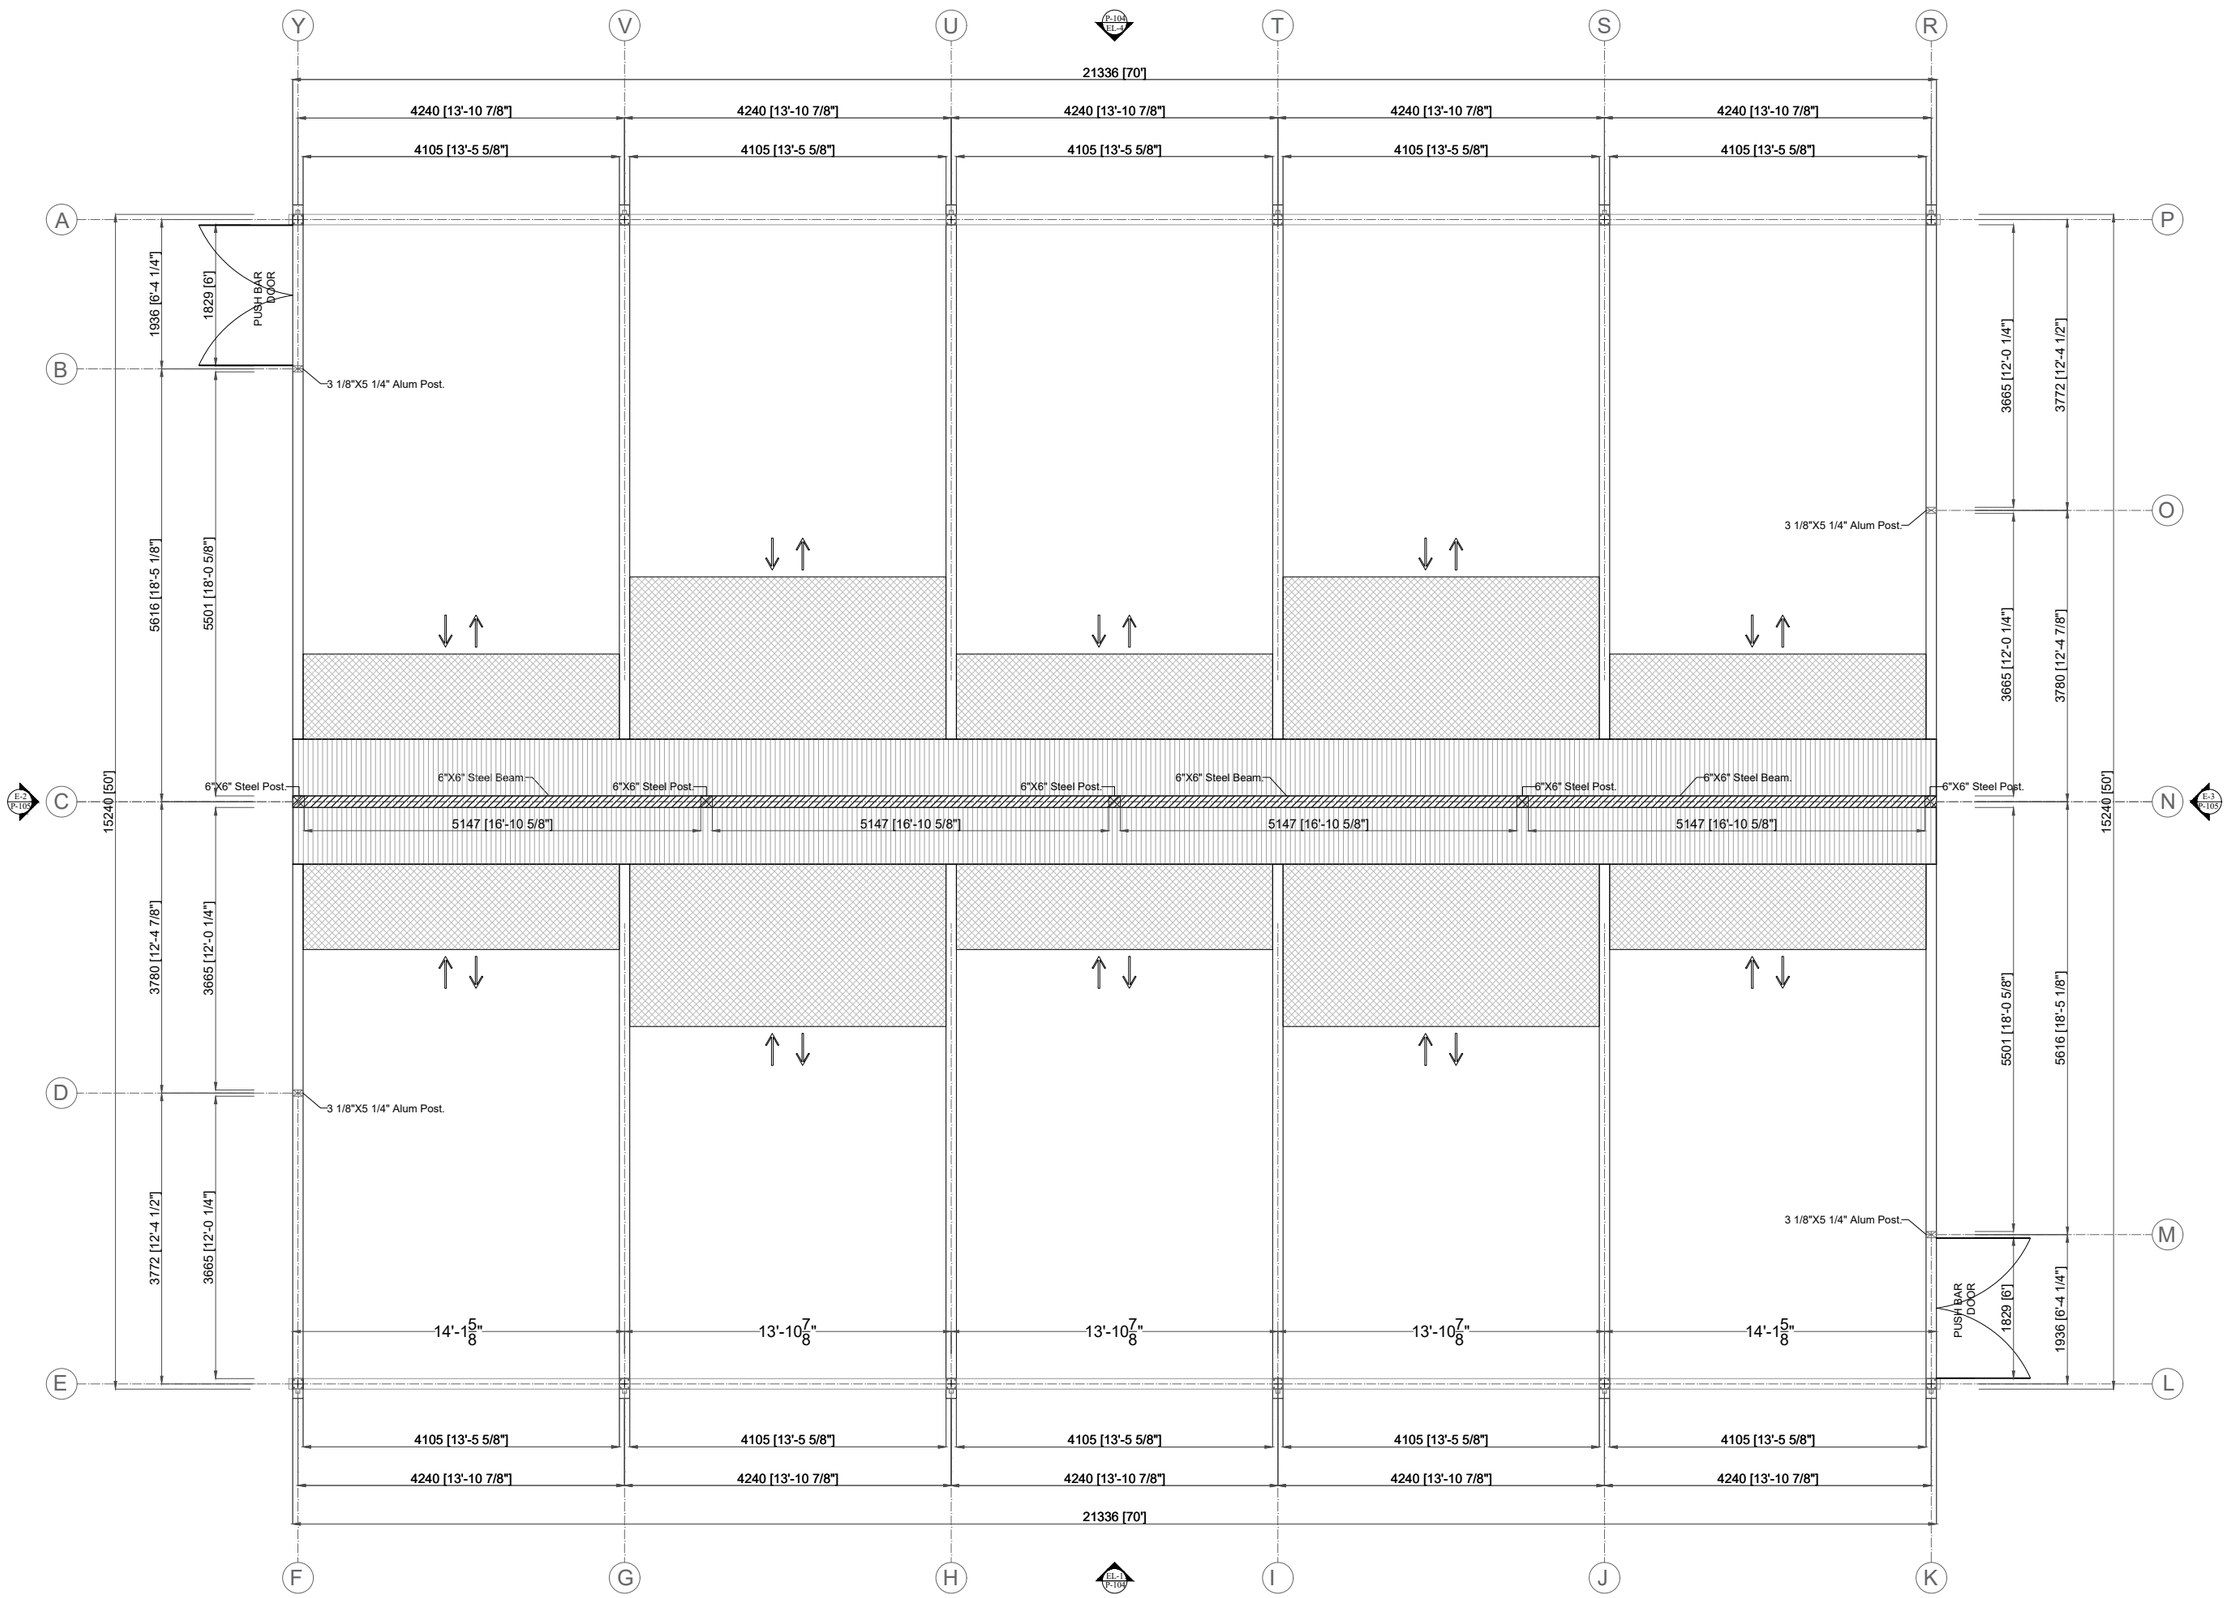

REVISIONS			
NO.	DESCRIPTION	DATE	BY

PREMIUM PERGOLA

CUSTOMER SIGNATURE:

DRAWN BY:

CHECKED BY:

Date: 12/23/2025

P-103

ELEVATION F-K

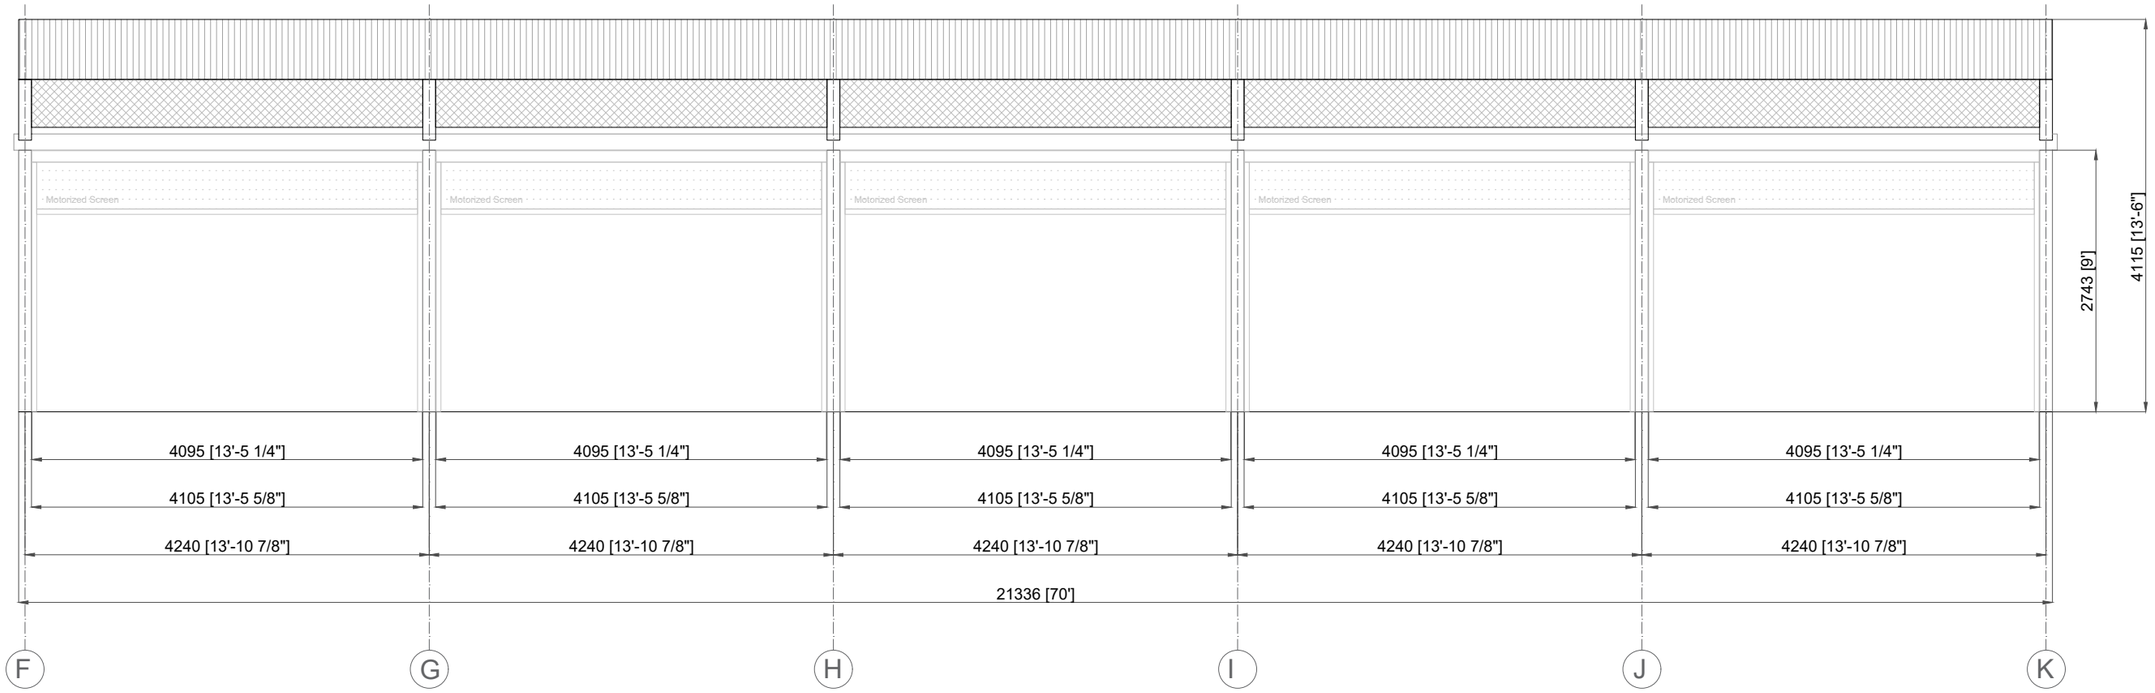

EL-1 P-104 ELEVATION

ELEVATION R-Y

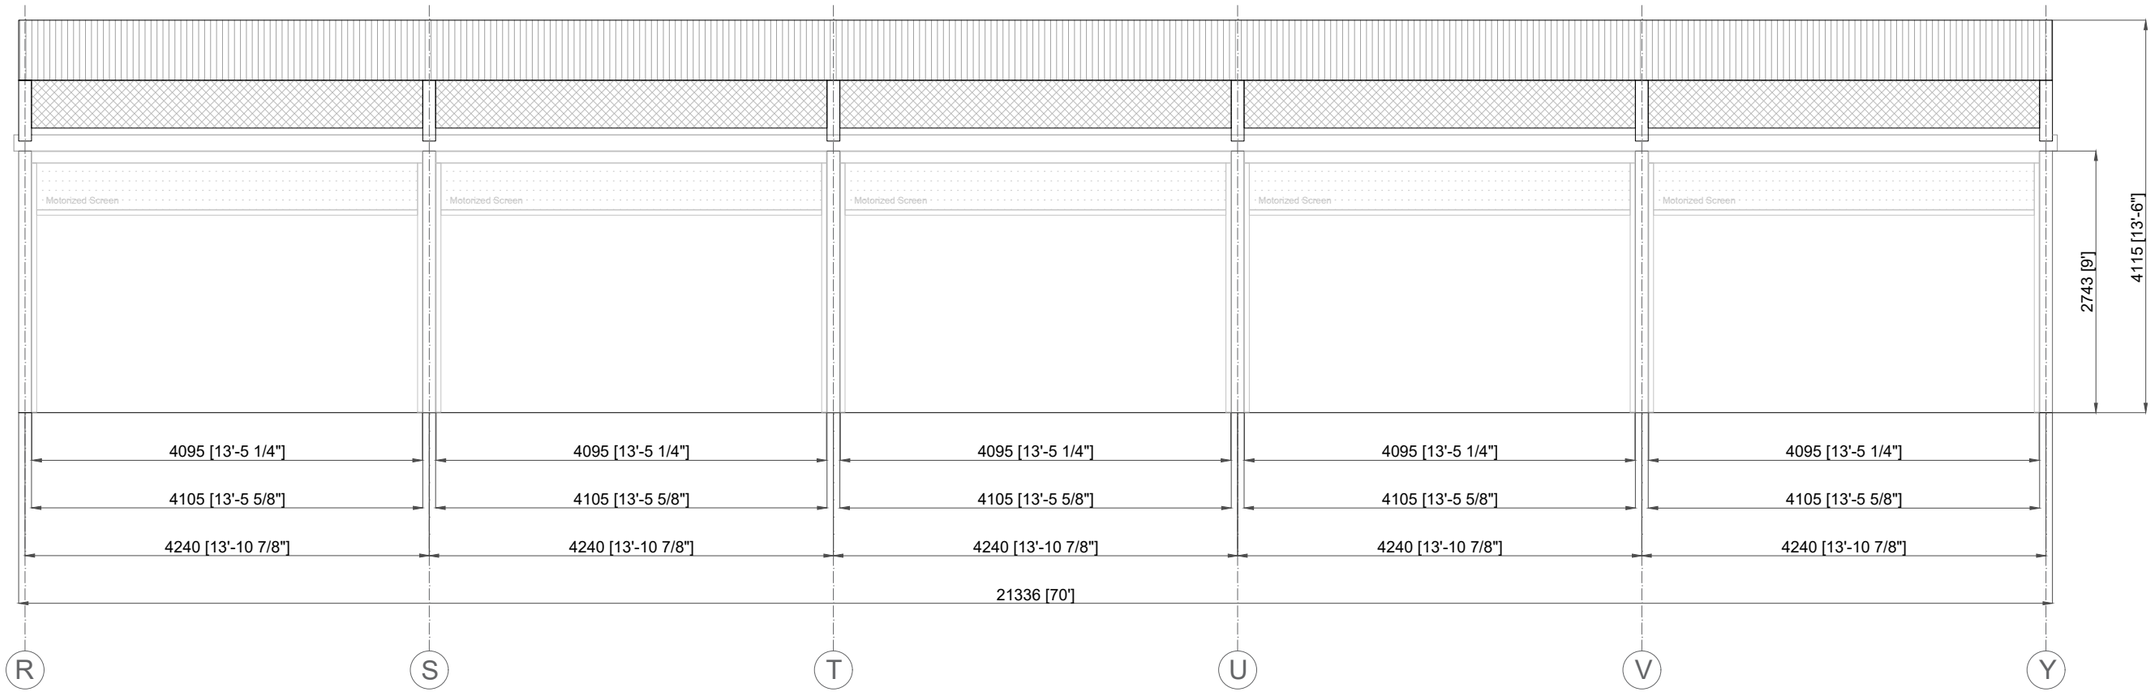

EL-4 P-104 ELEVATION

REVISIONS

NO.	DESCRIPTION	DATE	BY

PREMIUM PERGOLA

CUSTOMER SIGNATURE:

DRAWN BY:

CHECKED BY:

Date: 12/23/2025

P-104

ELEVATION A-E

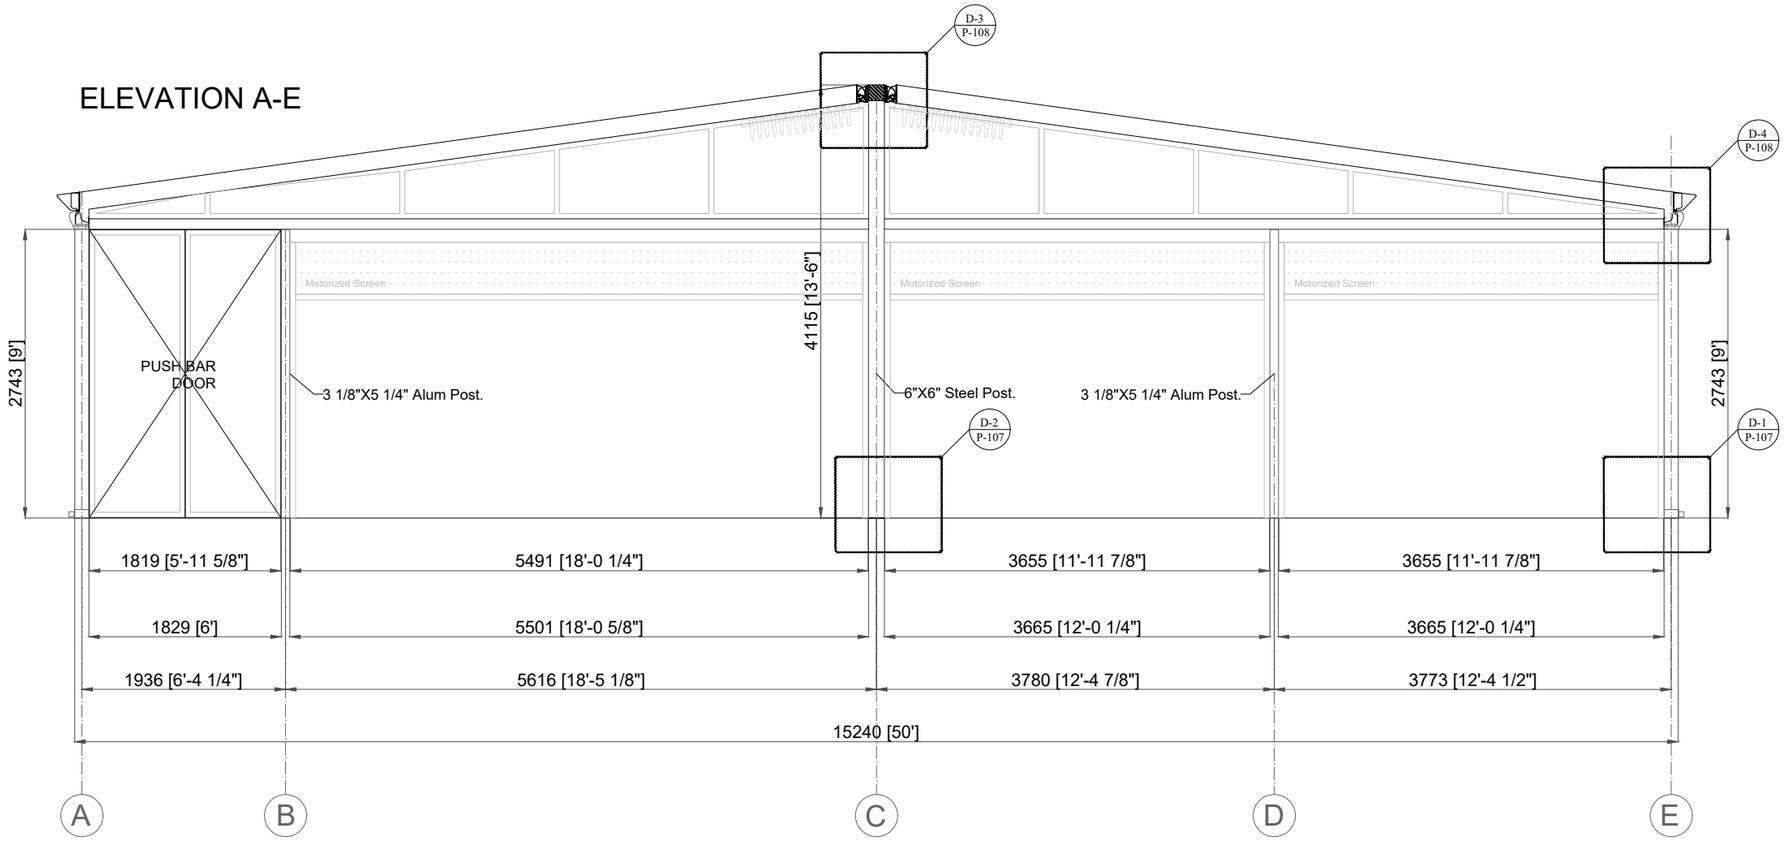

EL-2 / P-105 ELEVATION

ELEVATION L-P

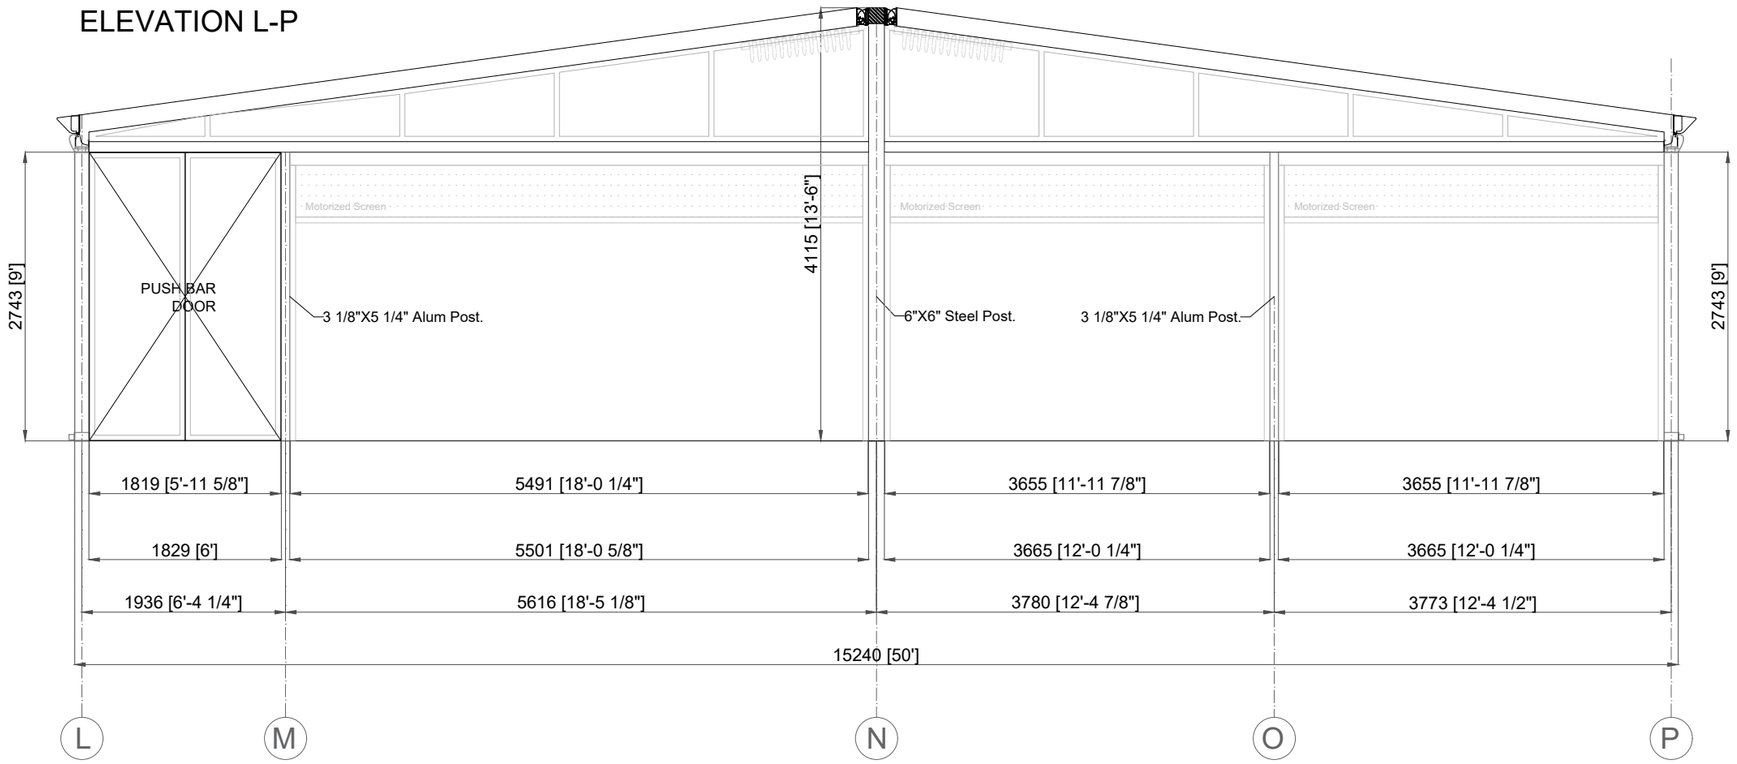

EL-3 / P-105 ELEVATION

REVISIONS

NO.	DESCRIPTION	DATE	BY

PREMIUM PERGOLA

CUSTOMER SIGNATURE:

DRAWN BY:

CHECKED BY:

Date: 12/23/2025

P-105

LIGHT PLAN

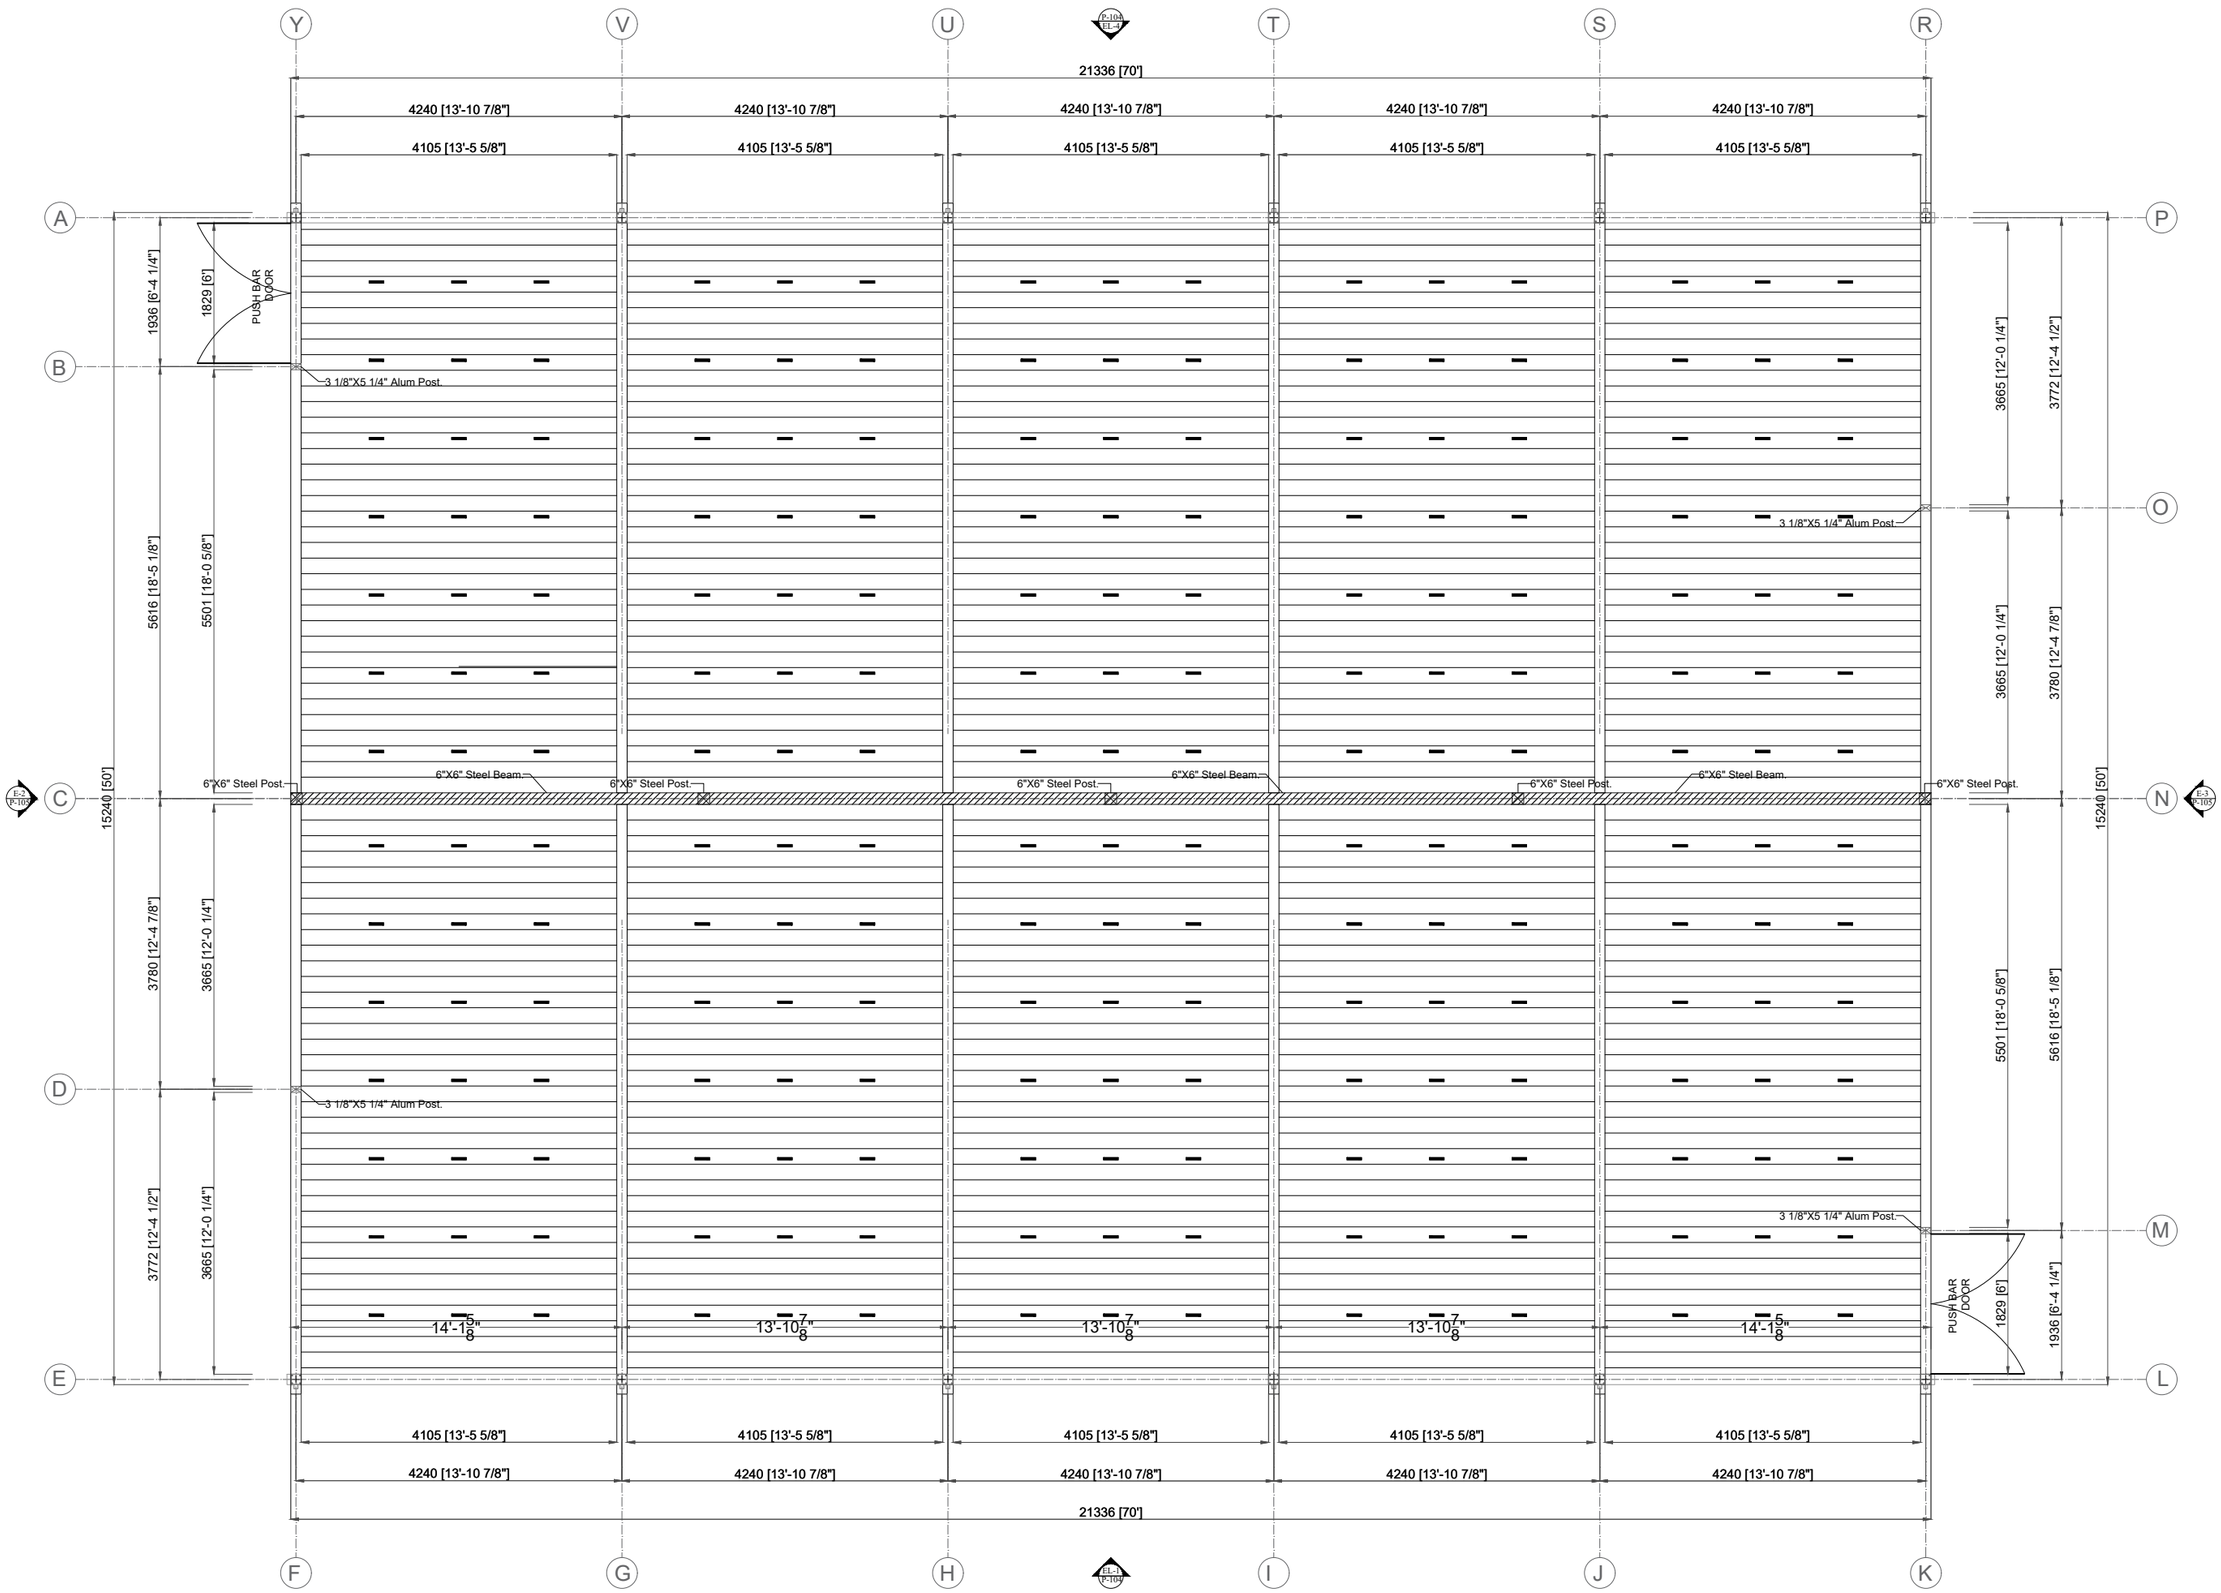

REVISIONS			
NO.	DESCRIPTION	DATE	BY

PREMIUM PERGOLA

CUSTOMER SIGNATURE:

DRAWN BY:

CHECKED BY:

Date: 12/23/2025

P-106

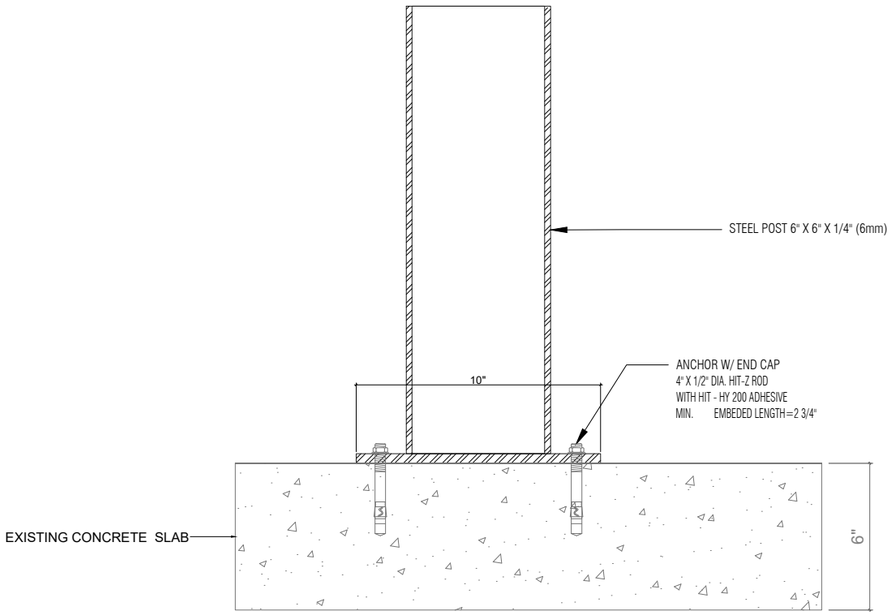

Steel Back Pillar Detail

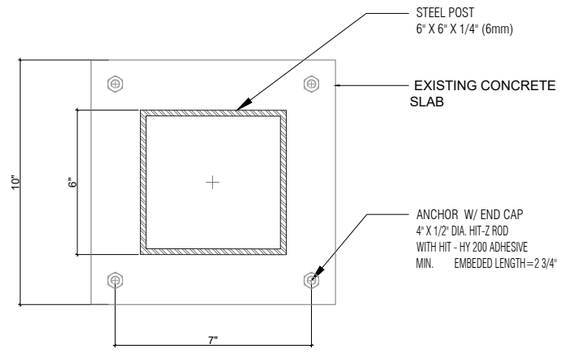

Steel Pillar Base Plate Detail

D-2
P-107
DETAIL

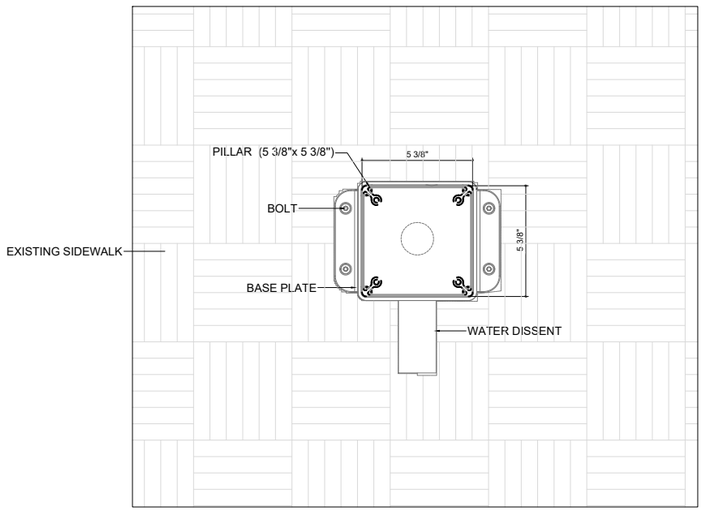

FOOTING PLAN

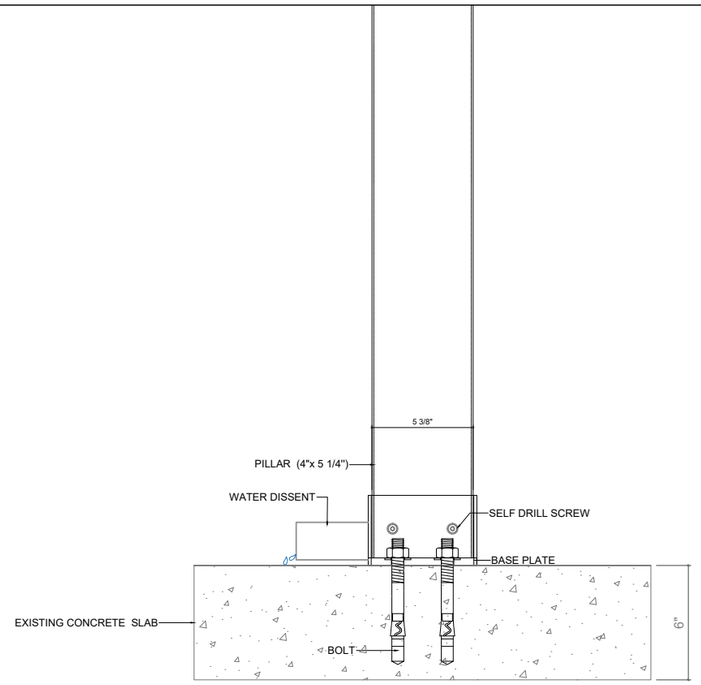

FOOTING DETAIL

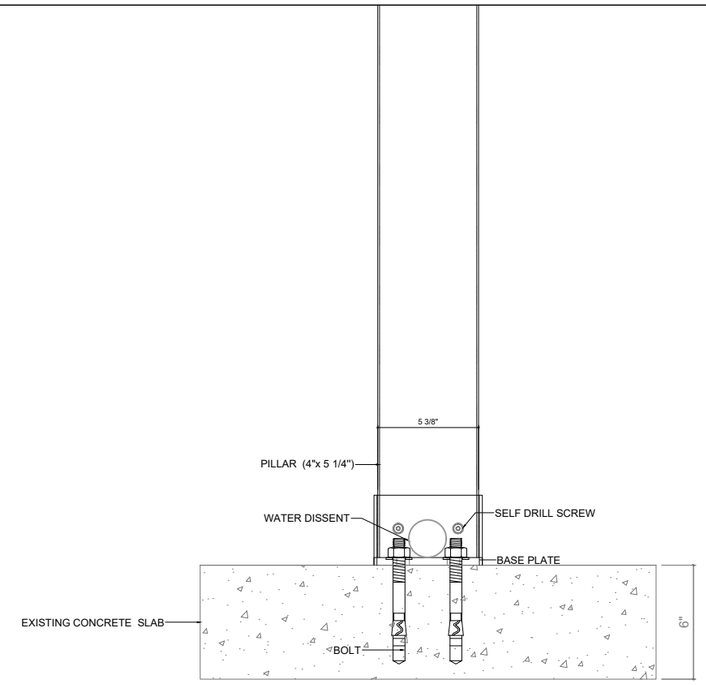

FOOTING DETAIL

D-1
P-107
DETAIL

REVISIONS

NO.	DESCRIPTION	DATE	BY

PREMIUM PERGOLA

CUSTOMER SIGNATURE:

DRAWN BY:

CHECKED BY:

Date: 12/23/2025

P-107

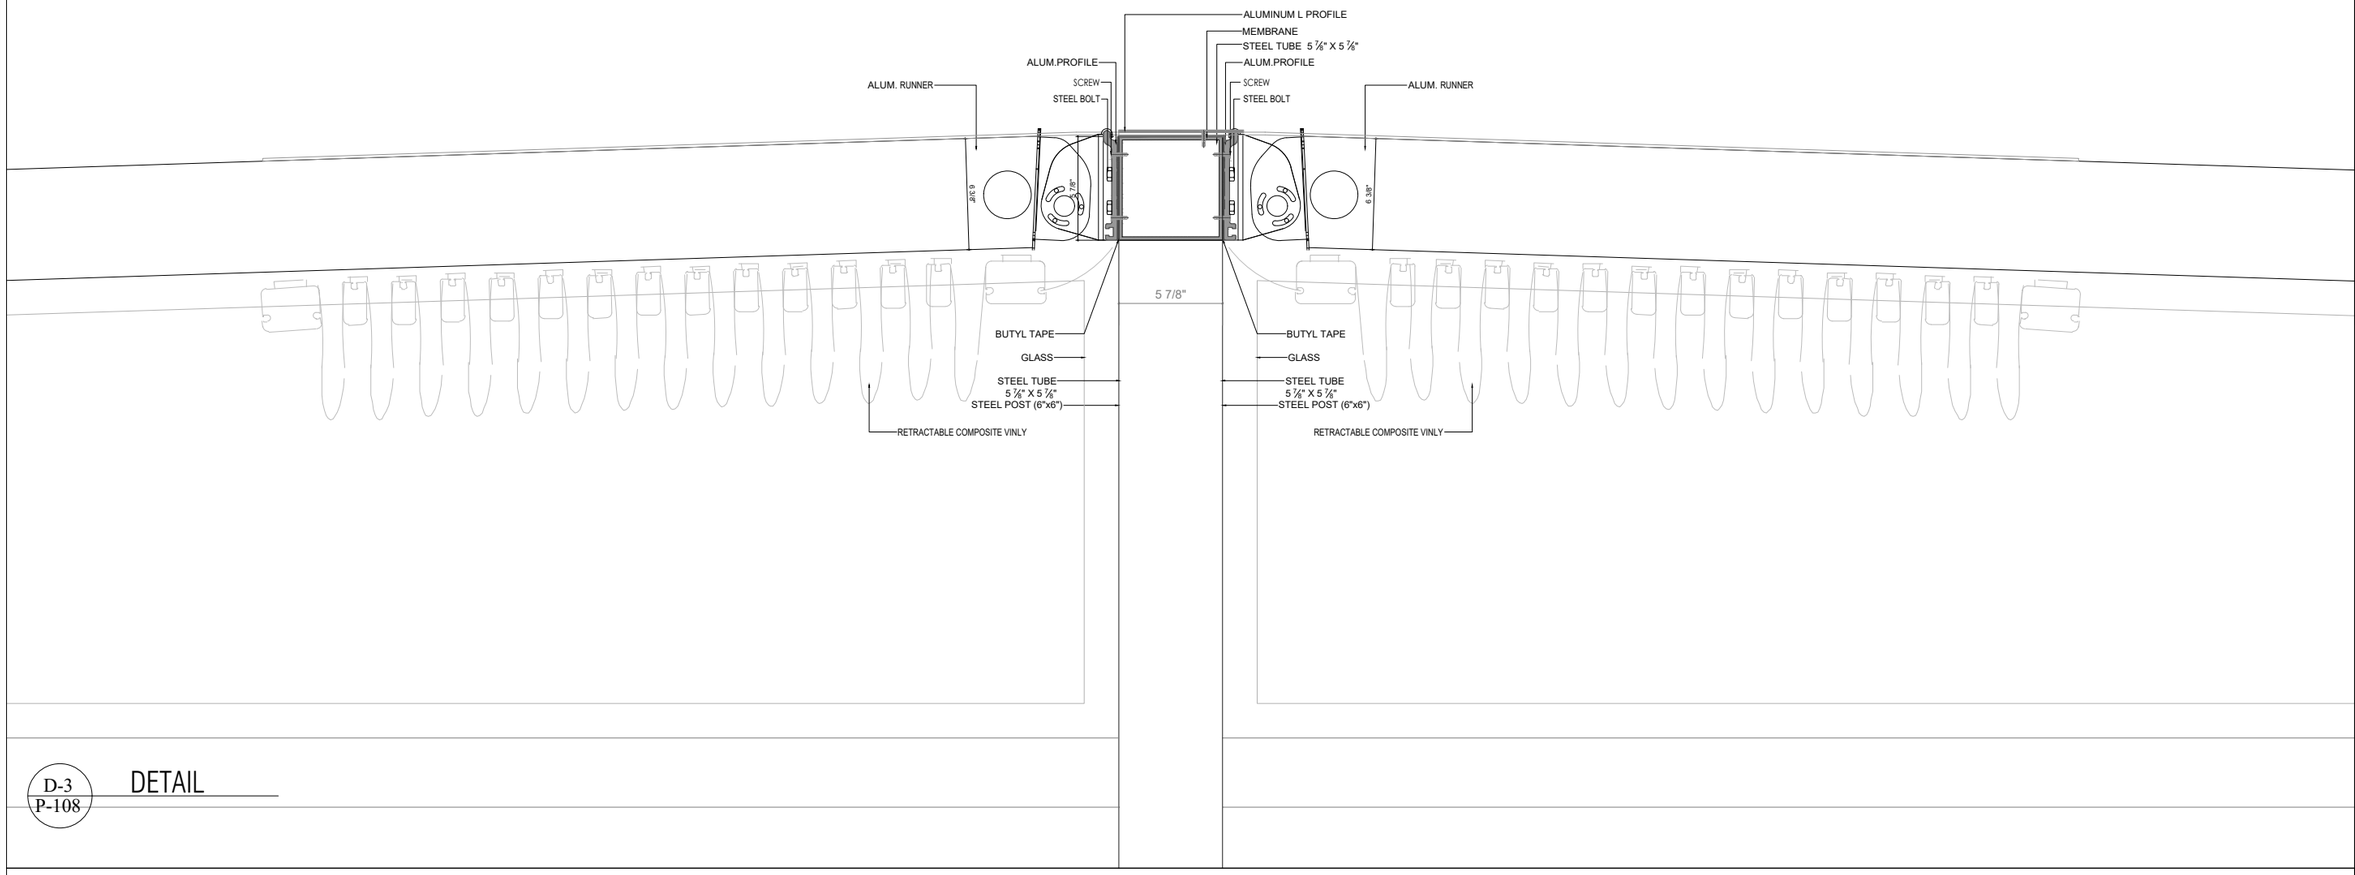

D-3
P-108

DETAIL

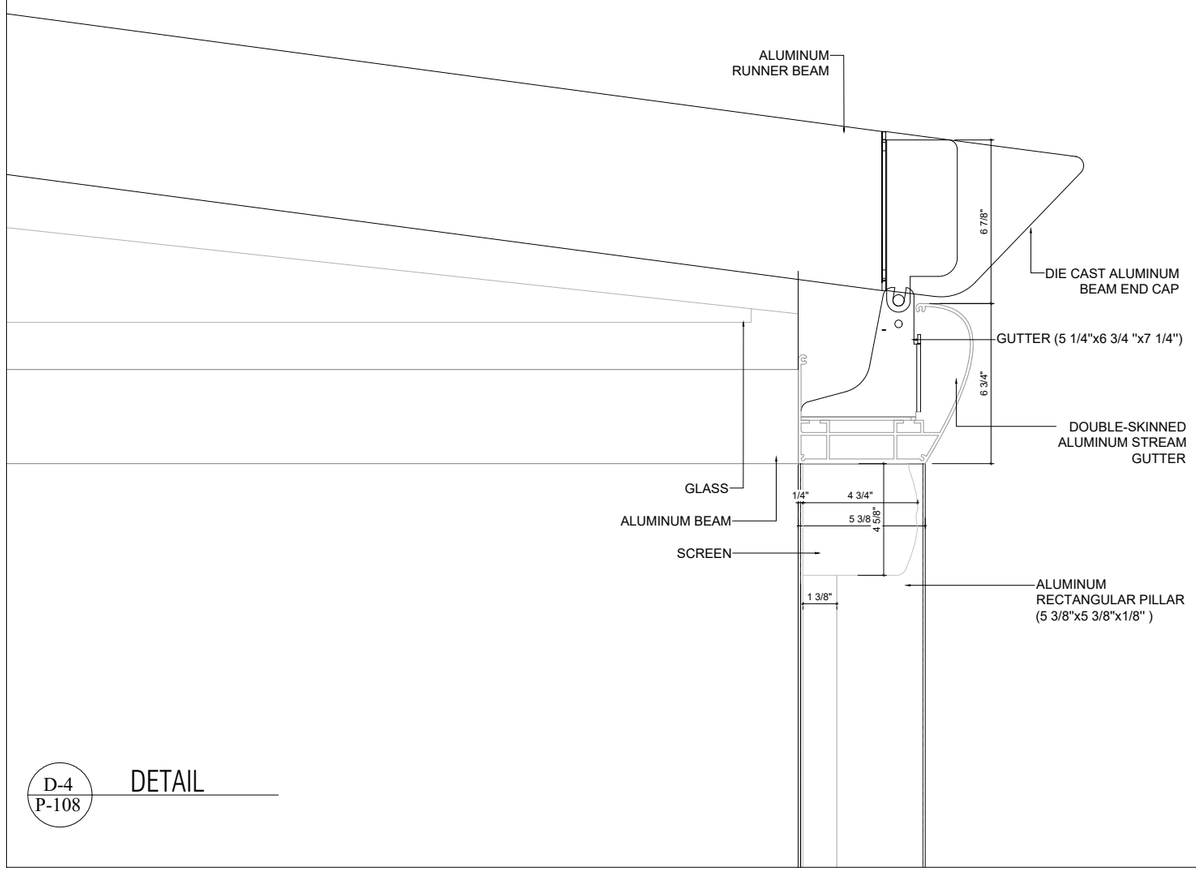

D-4
P-108

DETAIL

REVISIONS

NO.	DESCRIPTION	DATE	BY

PREMIUM PERGOLA

CUSTOMER SIGNATURE:

DRAWN BY:

CHECKED BY:

Date: 12/23/2025

P-108